


ARMATURA PALI Ø600 L = 6 m

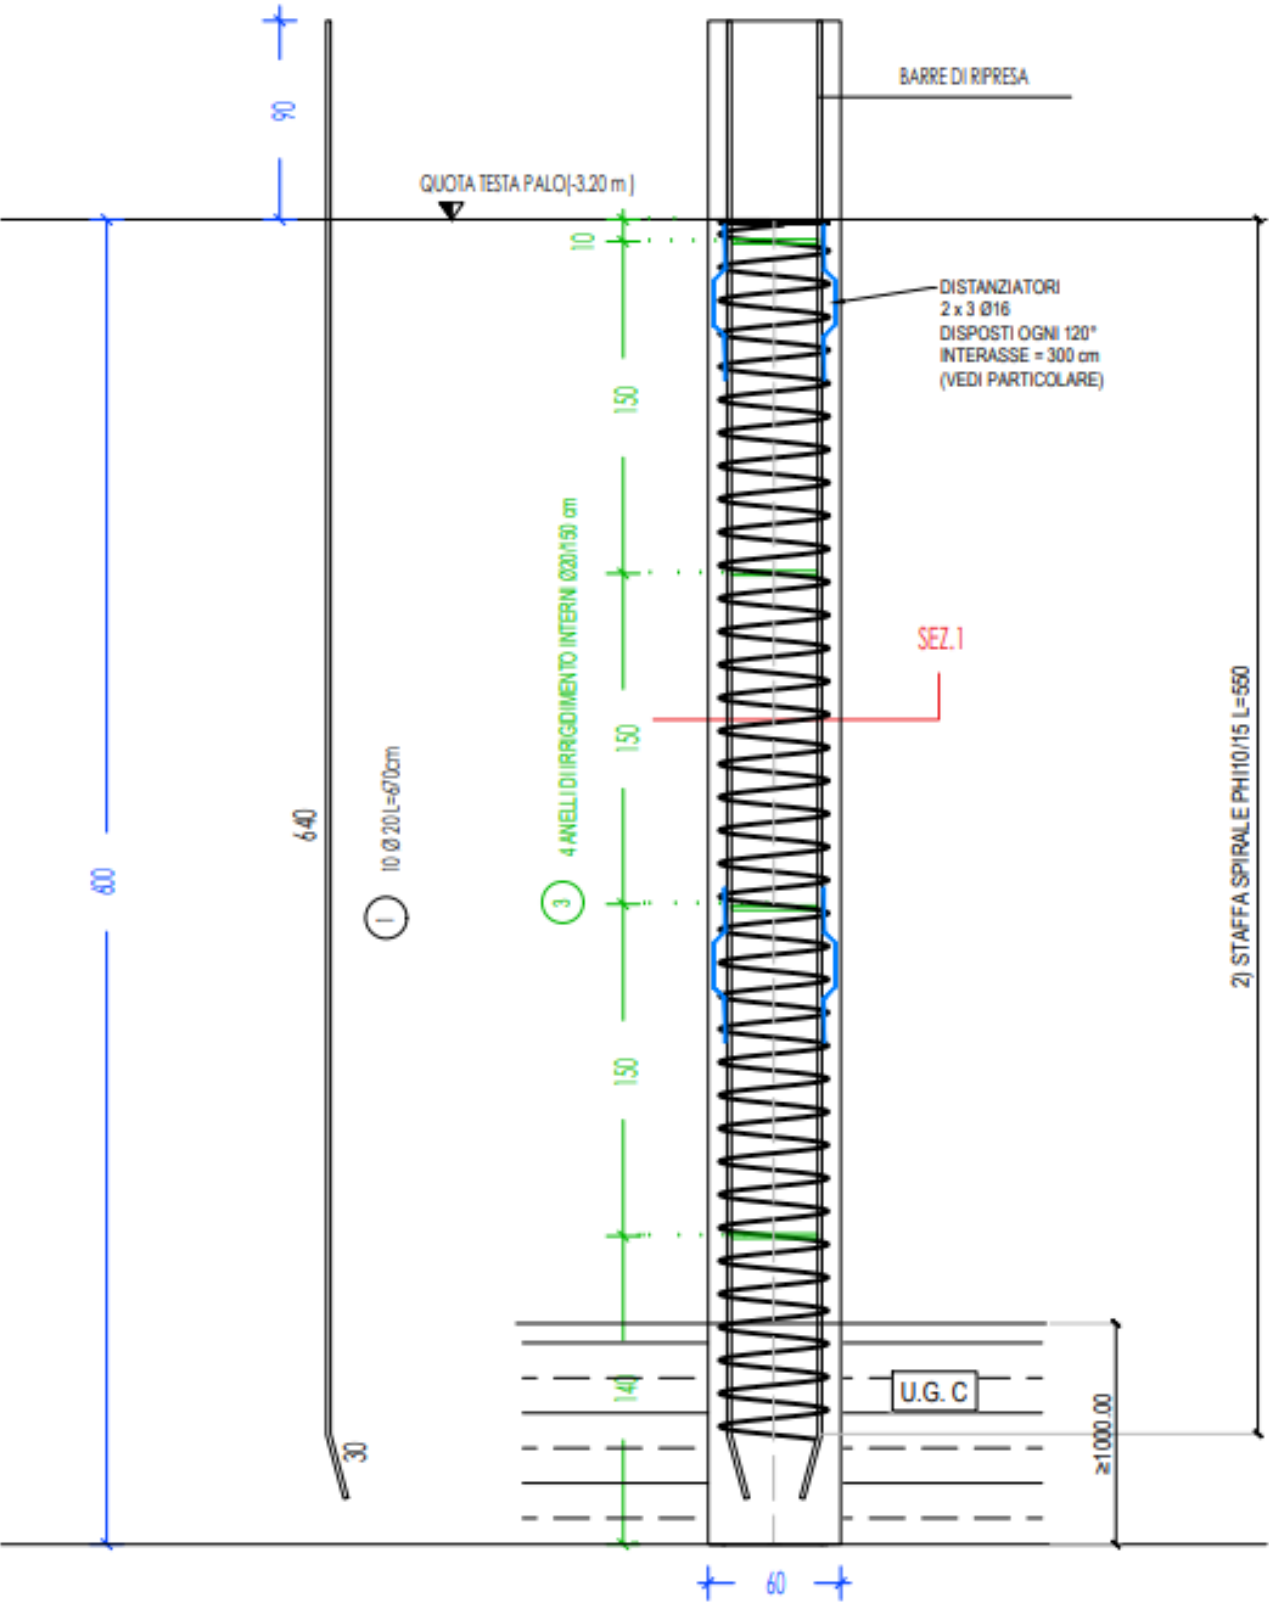

COORDINATE PALI

N. PALO	X	Y	ØPALO	L
	[m]	[m]	[mm]	[m]
81	512481.631	4349517.18	600	6

Quota testa palo (scapitozzatura): +51,70 m  
Quota imposta fondazione: + 50,80 m

