


ARMATURA PALI Ø600 L = 6 m

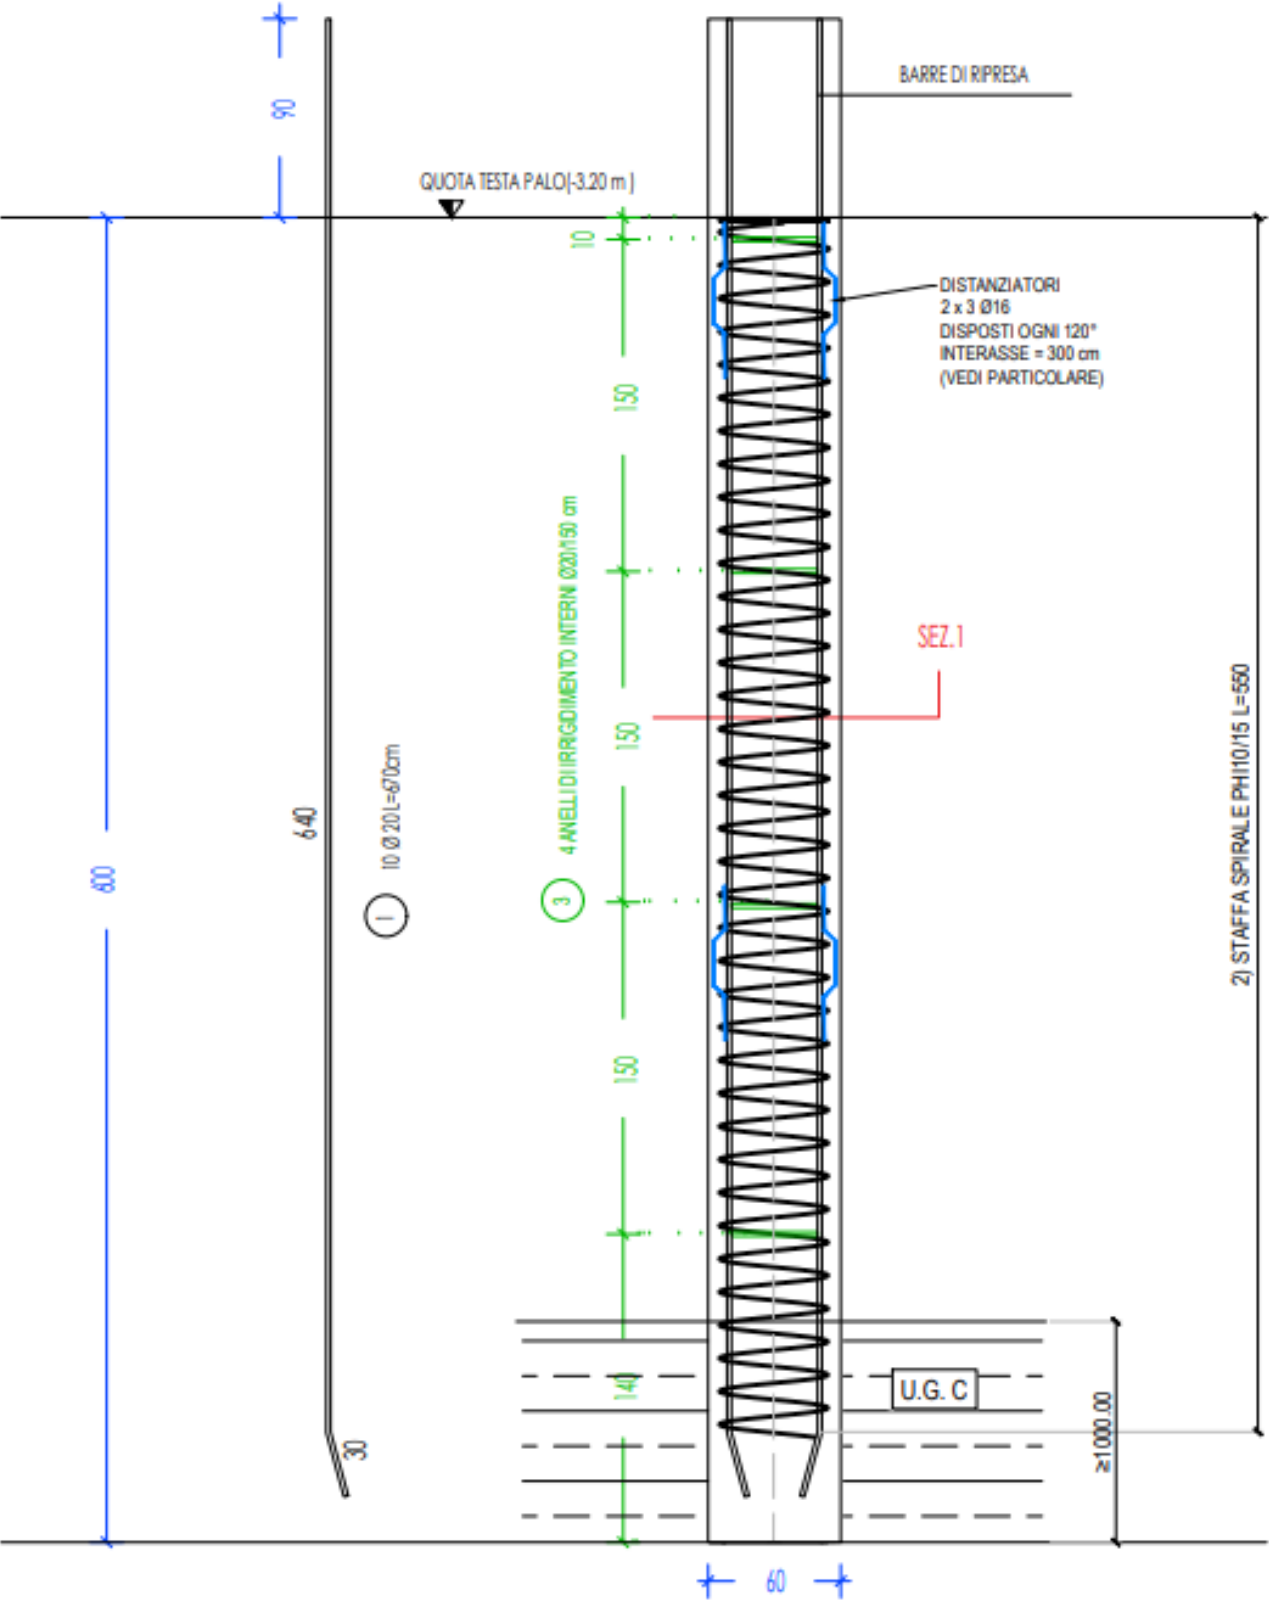

COORDINATE PALI

N. PALO	X [m]	Y [m]	ØPALO [mm]	L [m]
37	512460.212	4349537.55	600	6

Quota testa palo (scapitozzatura): +51,70 m

Quota imposta fondazione: + 50,80 m

