
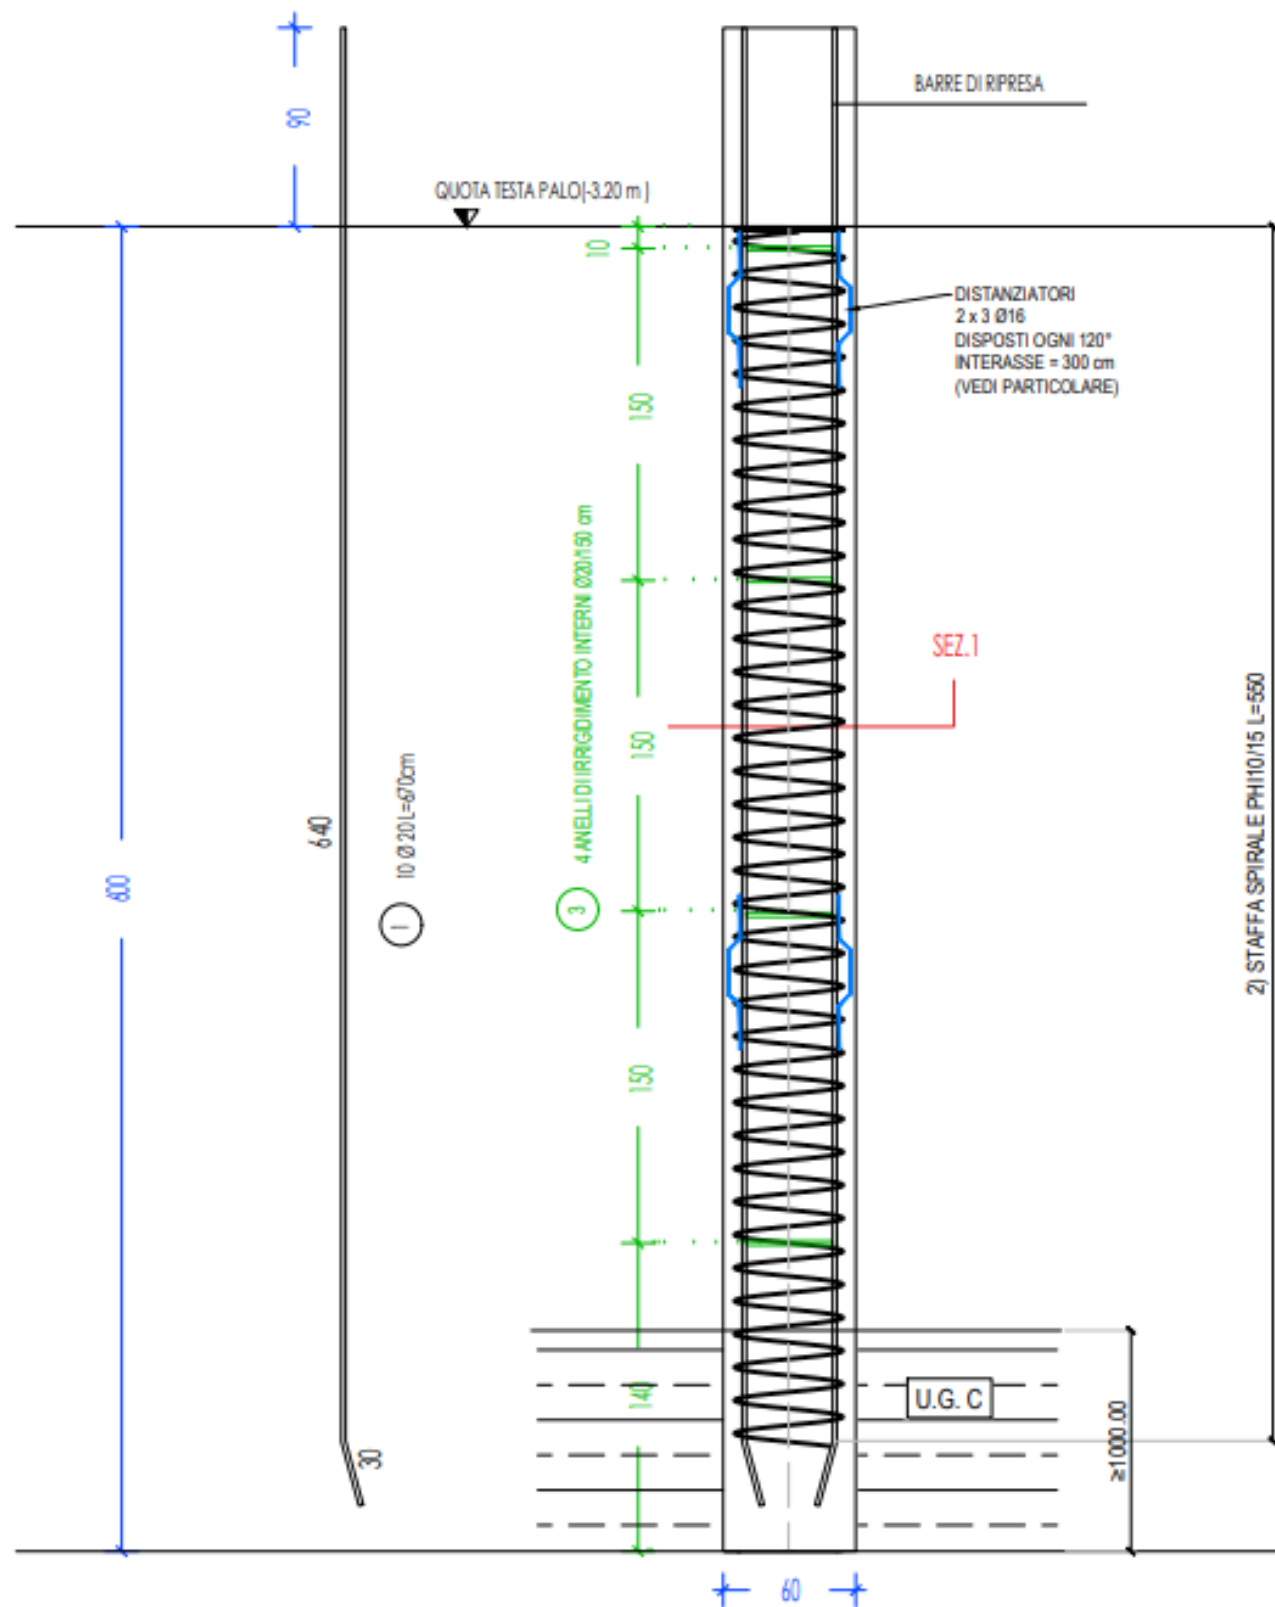


ARMATURA PALI Ø600 L = 6 m

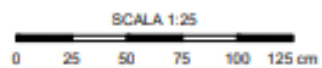

| COORDINATE PALI |            |           |       |     |
|-----------------|------------|-----------|-------|-----|
| N. PALO         | X          | Y         | ØPALO | L   |
|                 | [m]        | [m]       | [mm]  | [m] |
| 63              | 512469.158 | 4349538.5 | 600   | 6   |

Quota testa palo (scapitozzatura): +51,70 m

Quota imposta fondazione: + 50,80 m

