
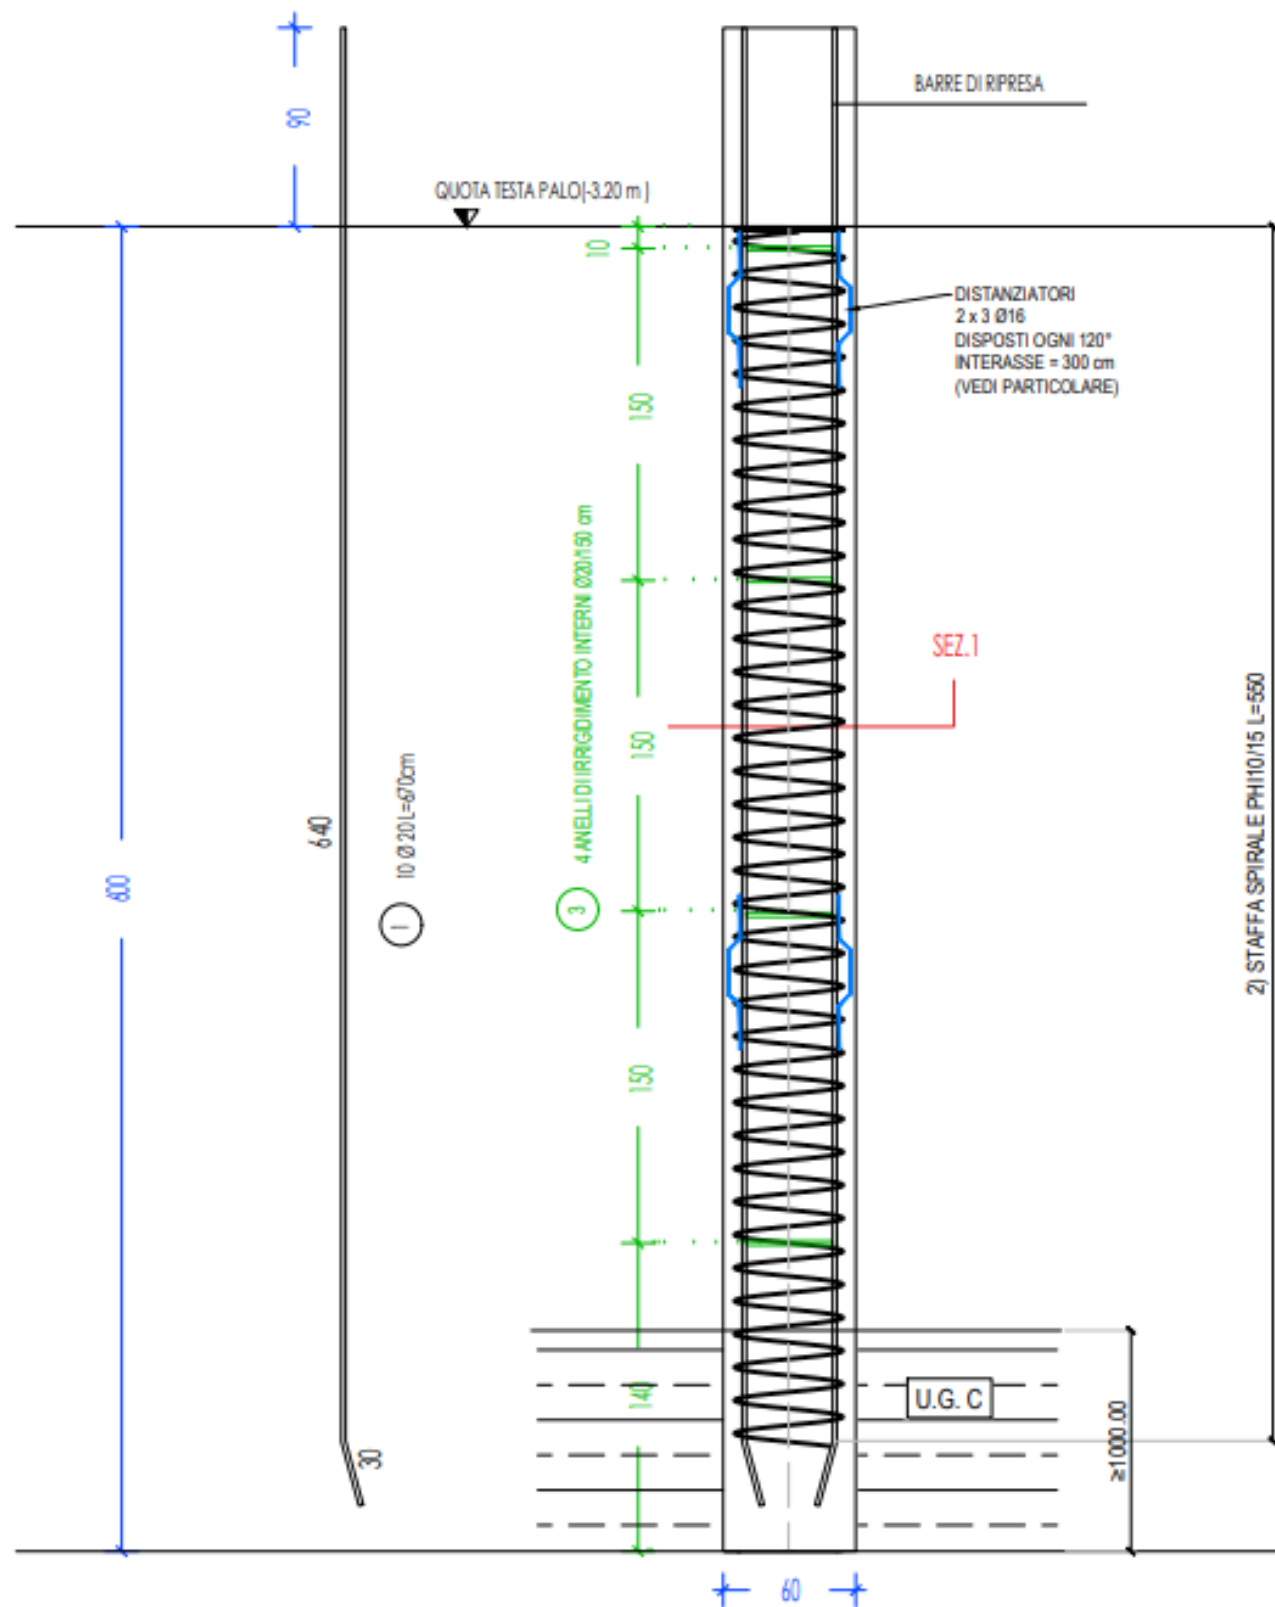


ARMATURA PALI Ø600 L = 6 m

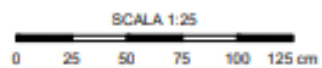


COORDINATE PALI

N. PALO	X	Y	ØPALO	L
	[m]	[m]	[mm]	[m]
14	512454.678	4349522.551	600	6

Quota testa palo (scapitozzatura): +51,70 m

Quota imposta fondazione: + 50,80 m

SEZIONE 1

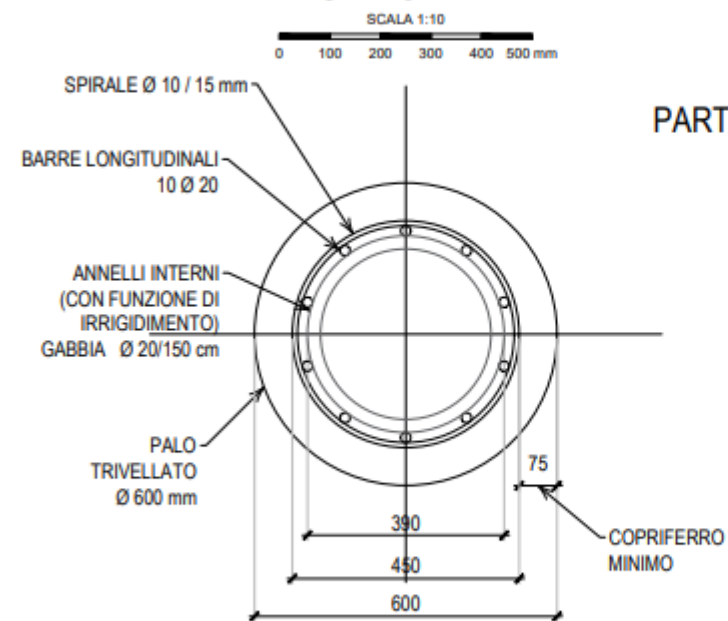

PARTICOLARE DISTANZIATORI

