

## ARMATURA PALI Ø600 L = 6 m

SCALA 1:25  
0 25 50 75 100 125 cm




## COORDINATE PALI

N. PALO	X [m]	Y [m]	ØPALO [mm]	L [m]
72	512477.395	4349531.15	600	6

Quota testa palo (scapitozzatura): +51,70 m  
Quota imposta fondazione: + 50,80 m

### SEZIONE 1

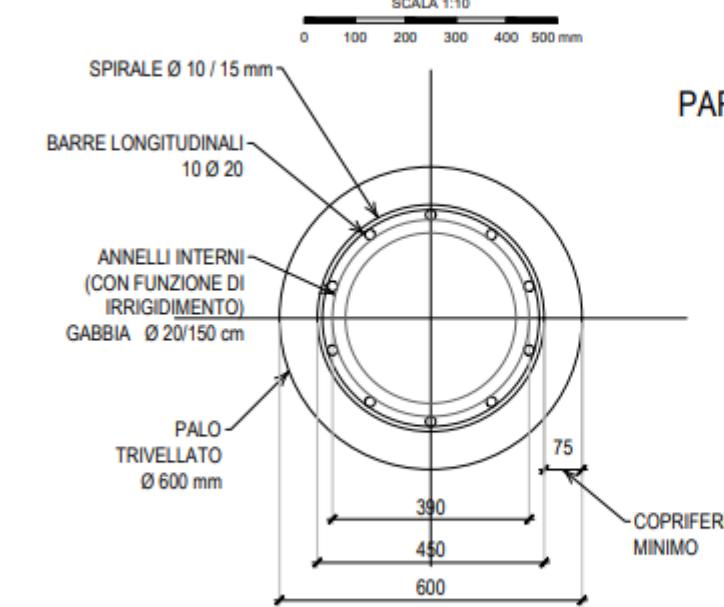

### PARTICOLARE DISTANZIATORI

