


ARMATURA PALI Ø600 L = 6 m

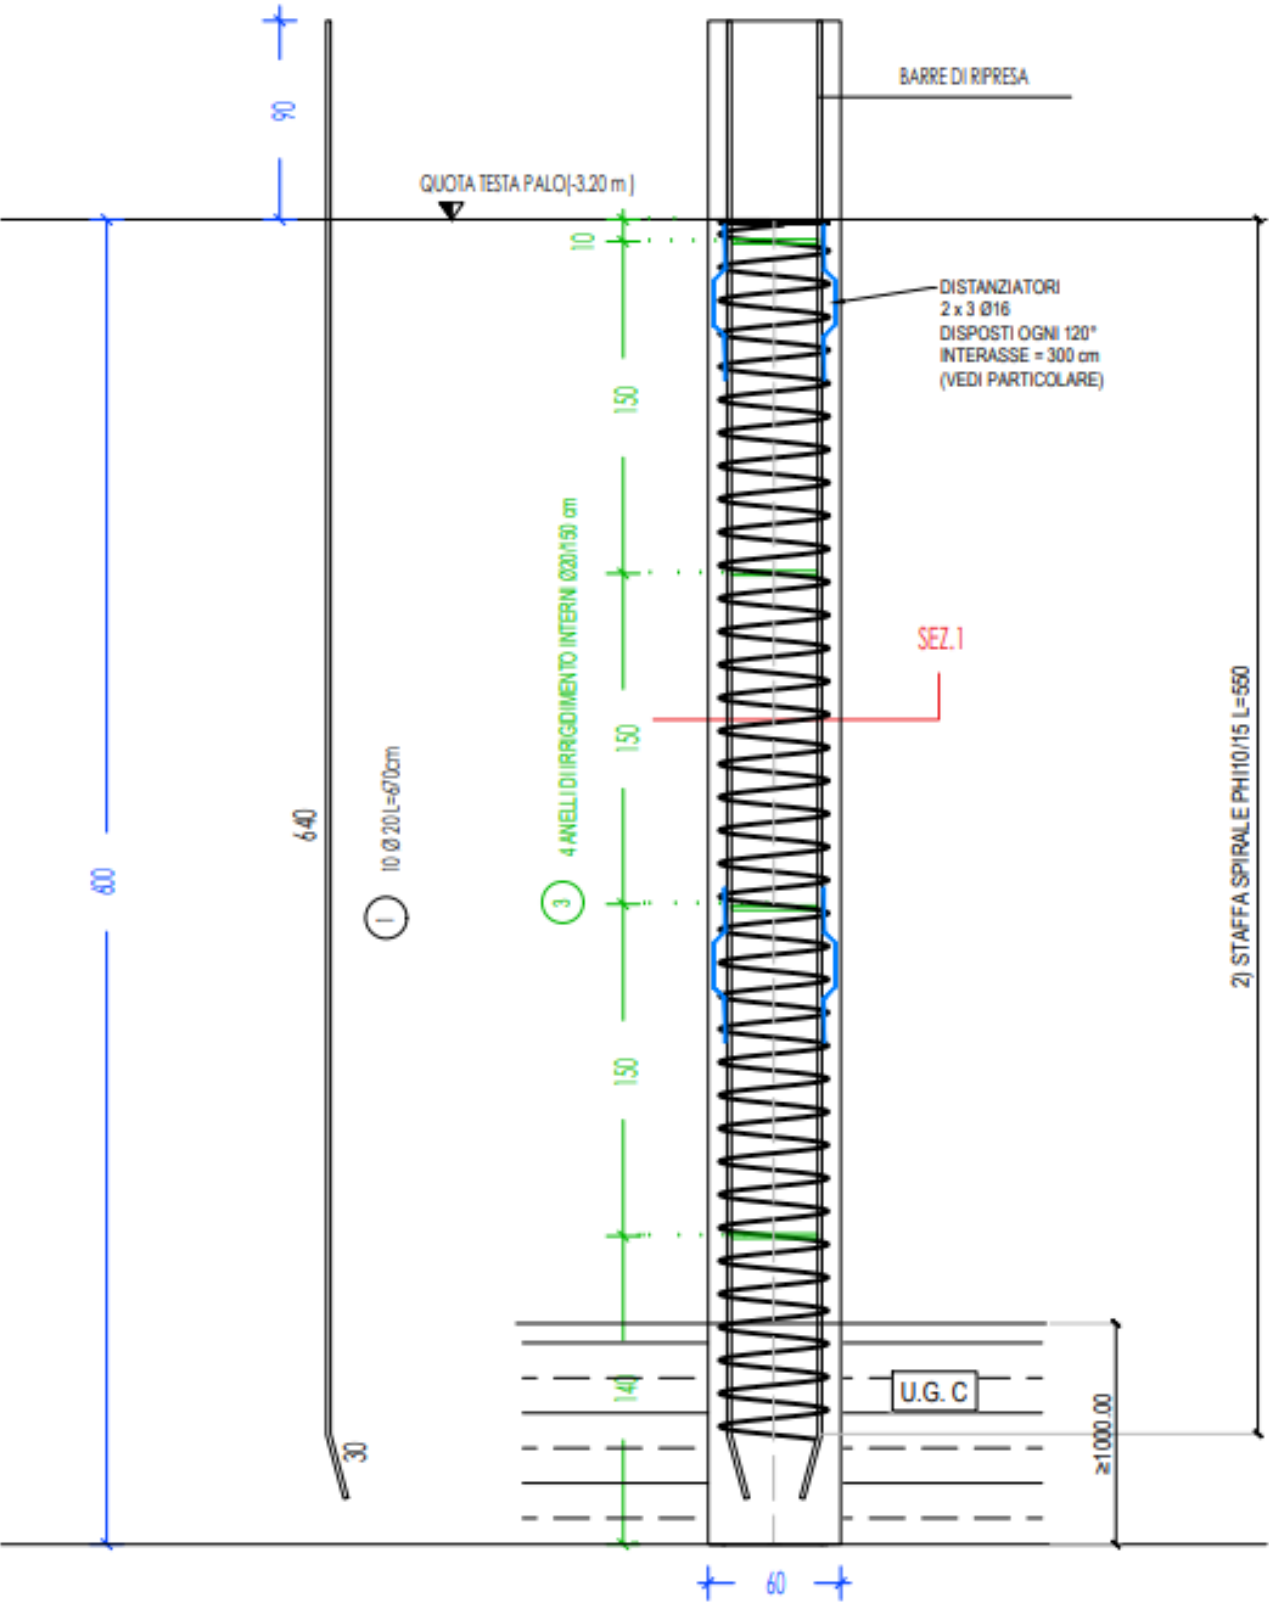


COORDINATE PALI

N. PALO	X	Y	ØPALO	L
	[m]	[m]	[mm]	[m]
3	512447.202	4349531.964	600	6

Quota testa palo (scapitozzatura): +51,70 m

Quota imposta fondazione: + 50,80 m

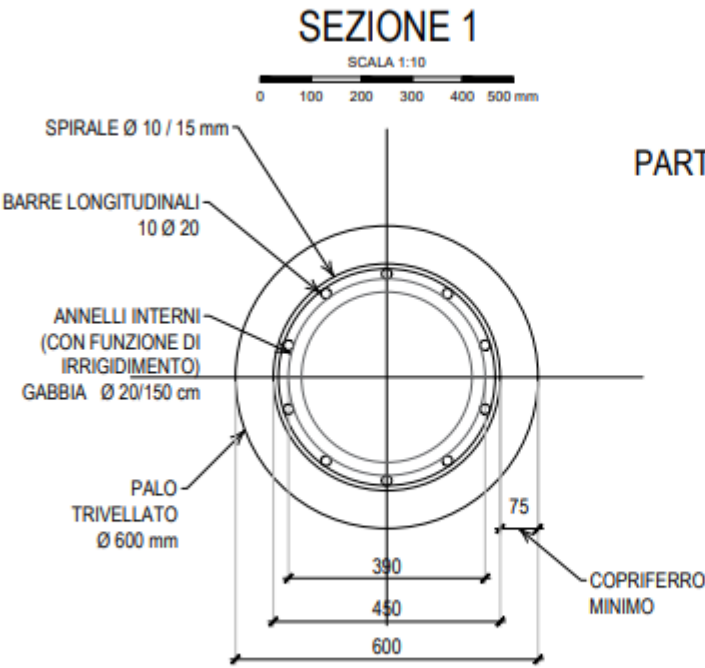

PARTICOLARE DISTANZIATORI



DISTANZIATORI  
Ø 16 L= 55 cm