


ARMATURA PALI Ø600 L = 6 m

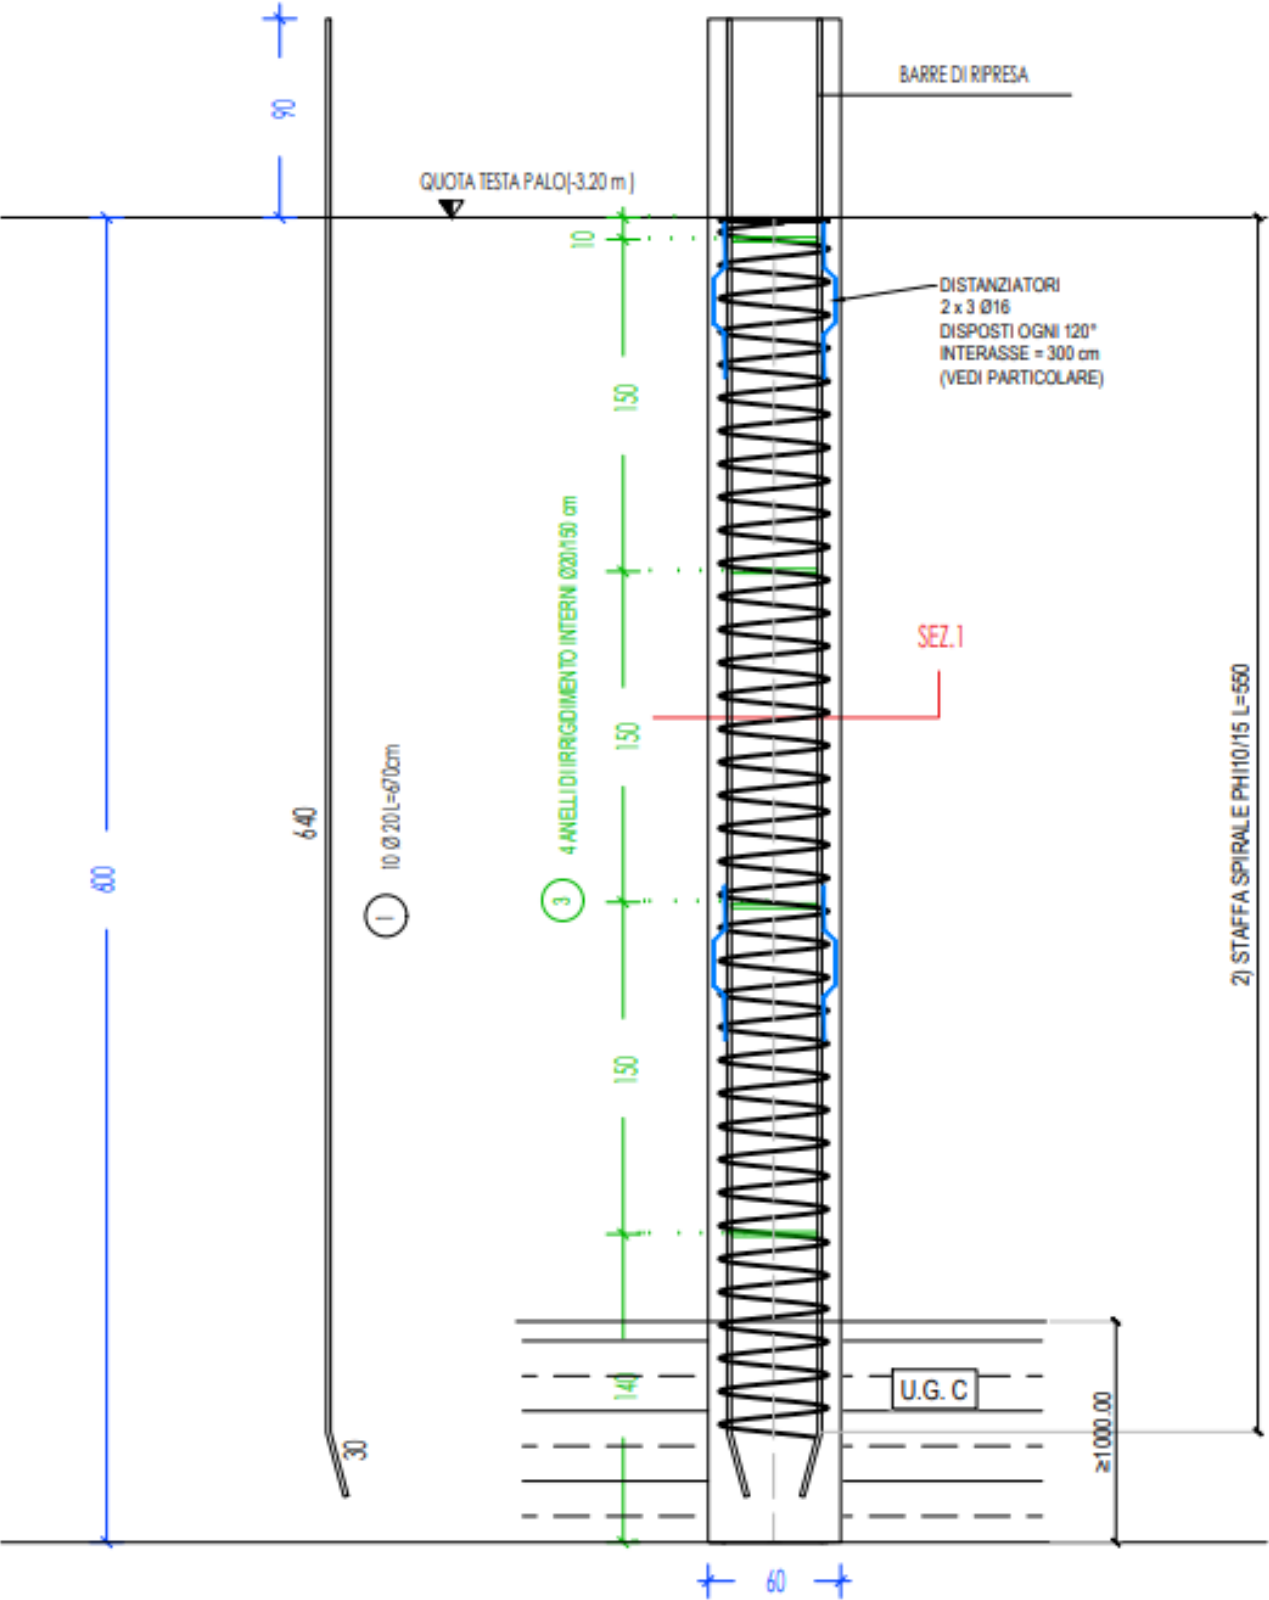

COORDINATE PALI

N. PALO	X [m]	Y [m]	ØPALO [mm]	L [m]
76	512478.046	4349523.31	600	6

Quota testa palo (scapitozzatura): +51,70 m
Quota imposta fondazione: + 50,80 m

