


ARMATURA PALI Ø600 L = 6 m

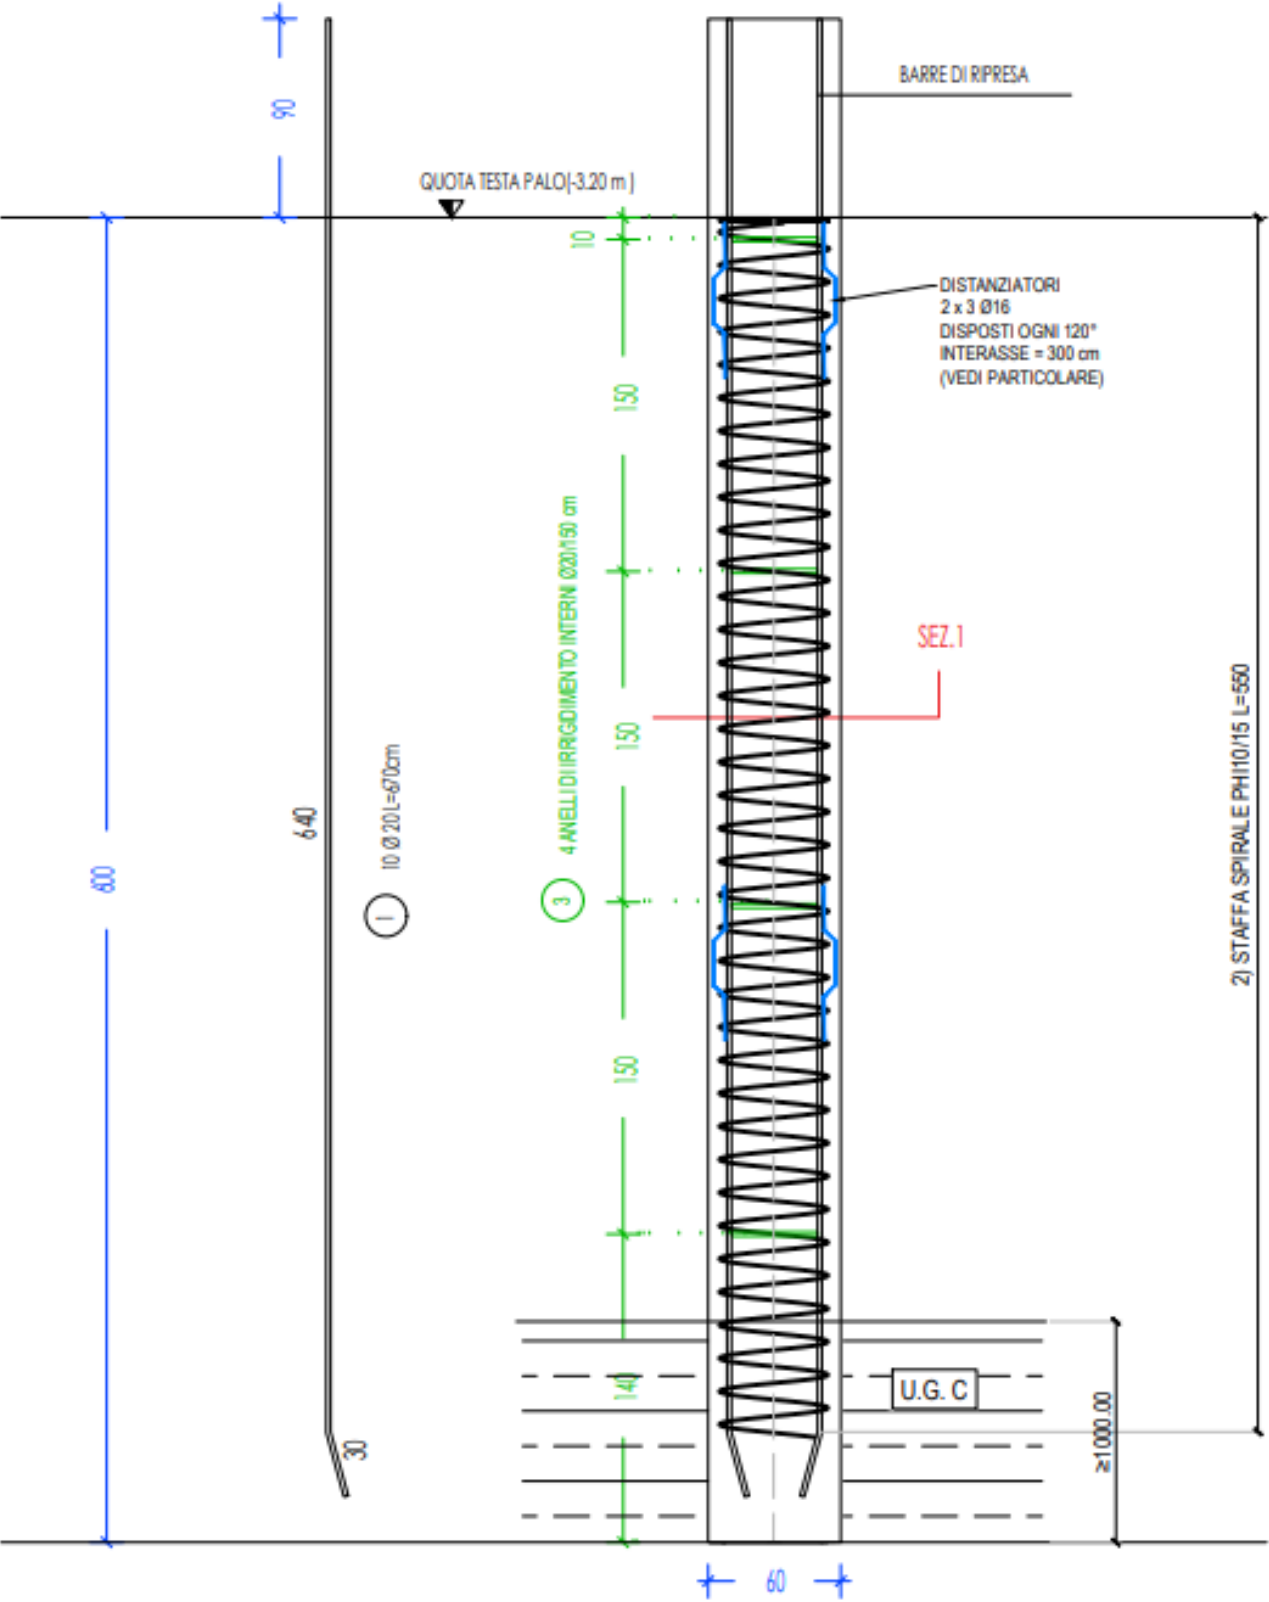

COORDINATE PALI

N. PALO	X	Y	ØPALO	L
	[m]	[m]	[mm]	[m]
107	512489.943	4349527.43	600	6

Quota testa palo (scapitozzatura): +51,70 m
Quota imposta fondazione: + 50,80 m

