
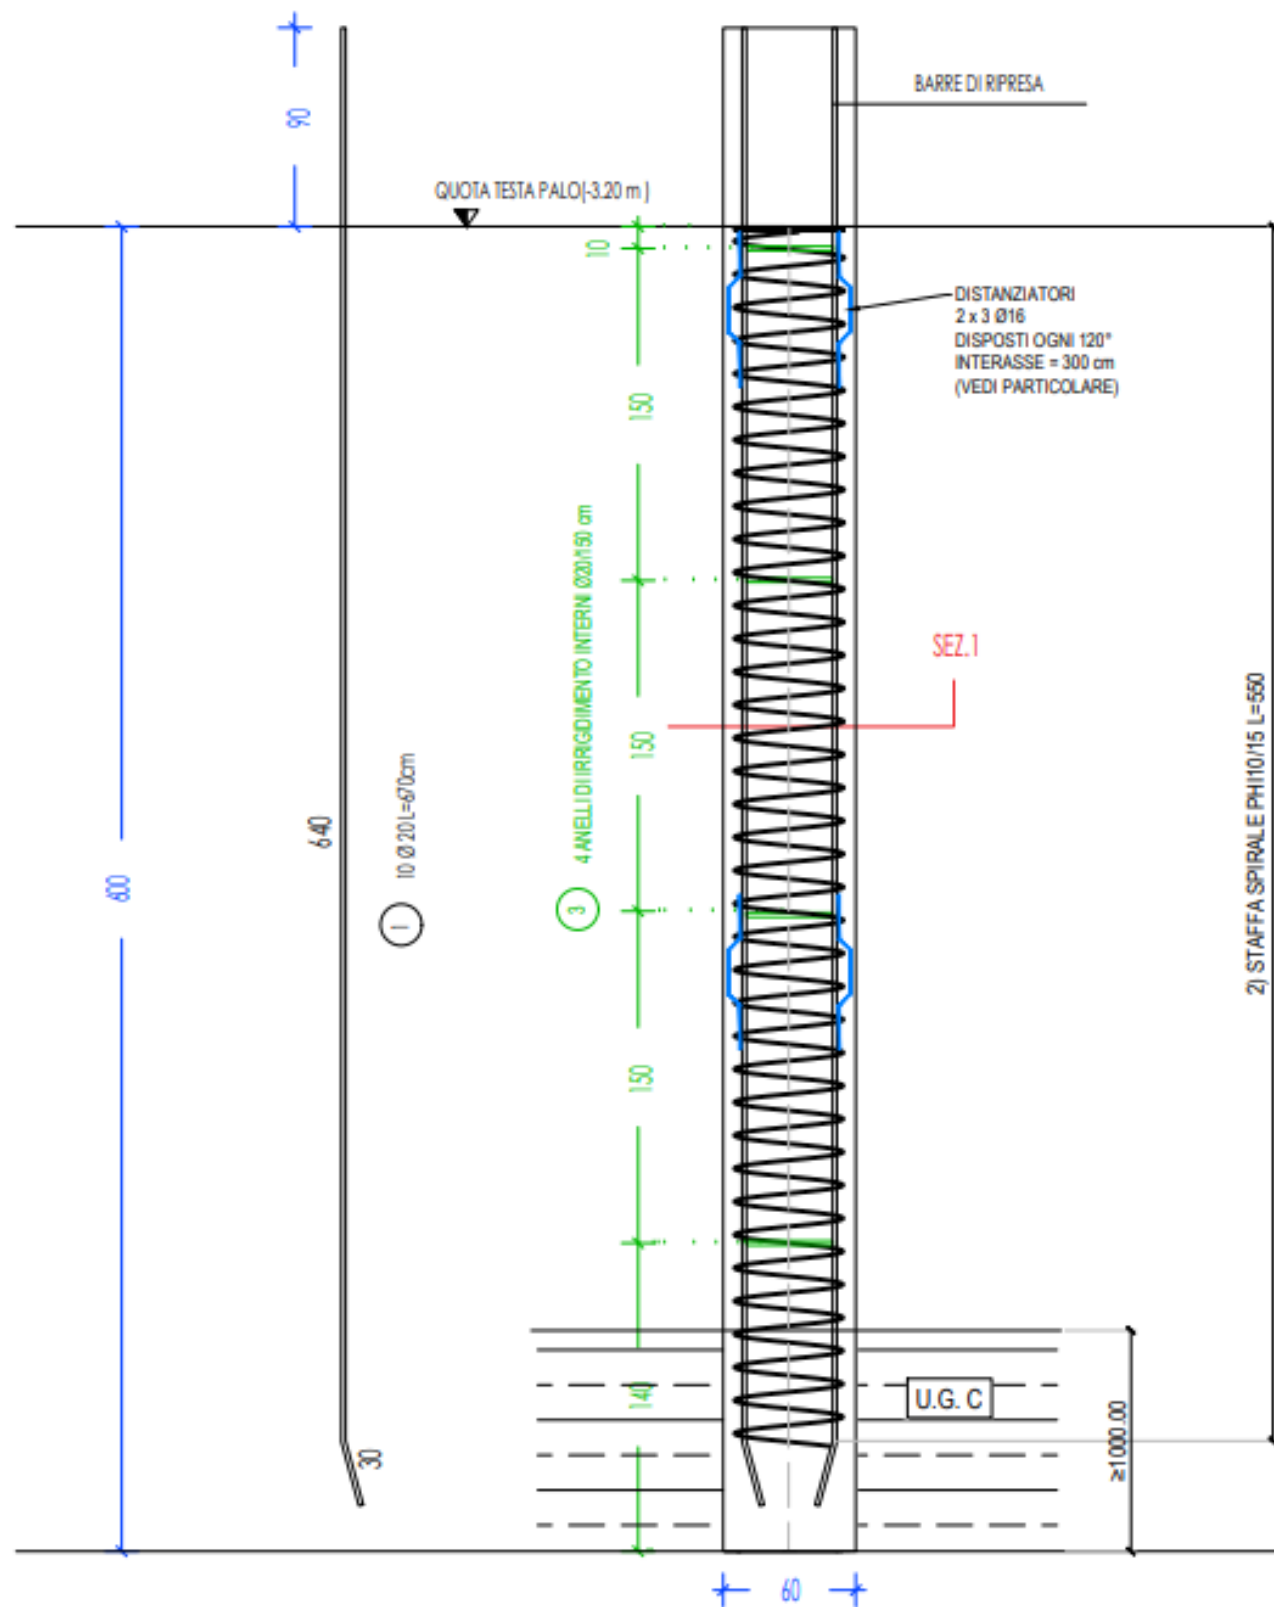


ARMATURA PALI Ø600 L = 6 m

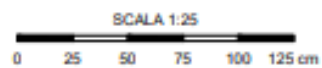

| COORDINATE PALI | | | | |
|-----------------|-----------|------------|-------|-----|
| N. PALO | X | Y | ØPALO | L |
| | [m] | [m] | [mm] | [m] |
| 61 | 512467.29 | 4349541.69 | 600 | 6 |

Quota testa palo (scapitozzatura): +51,70 m

Quota imposta fondazione: + 50,80 m

