
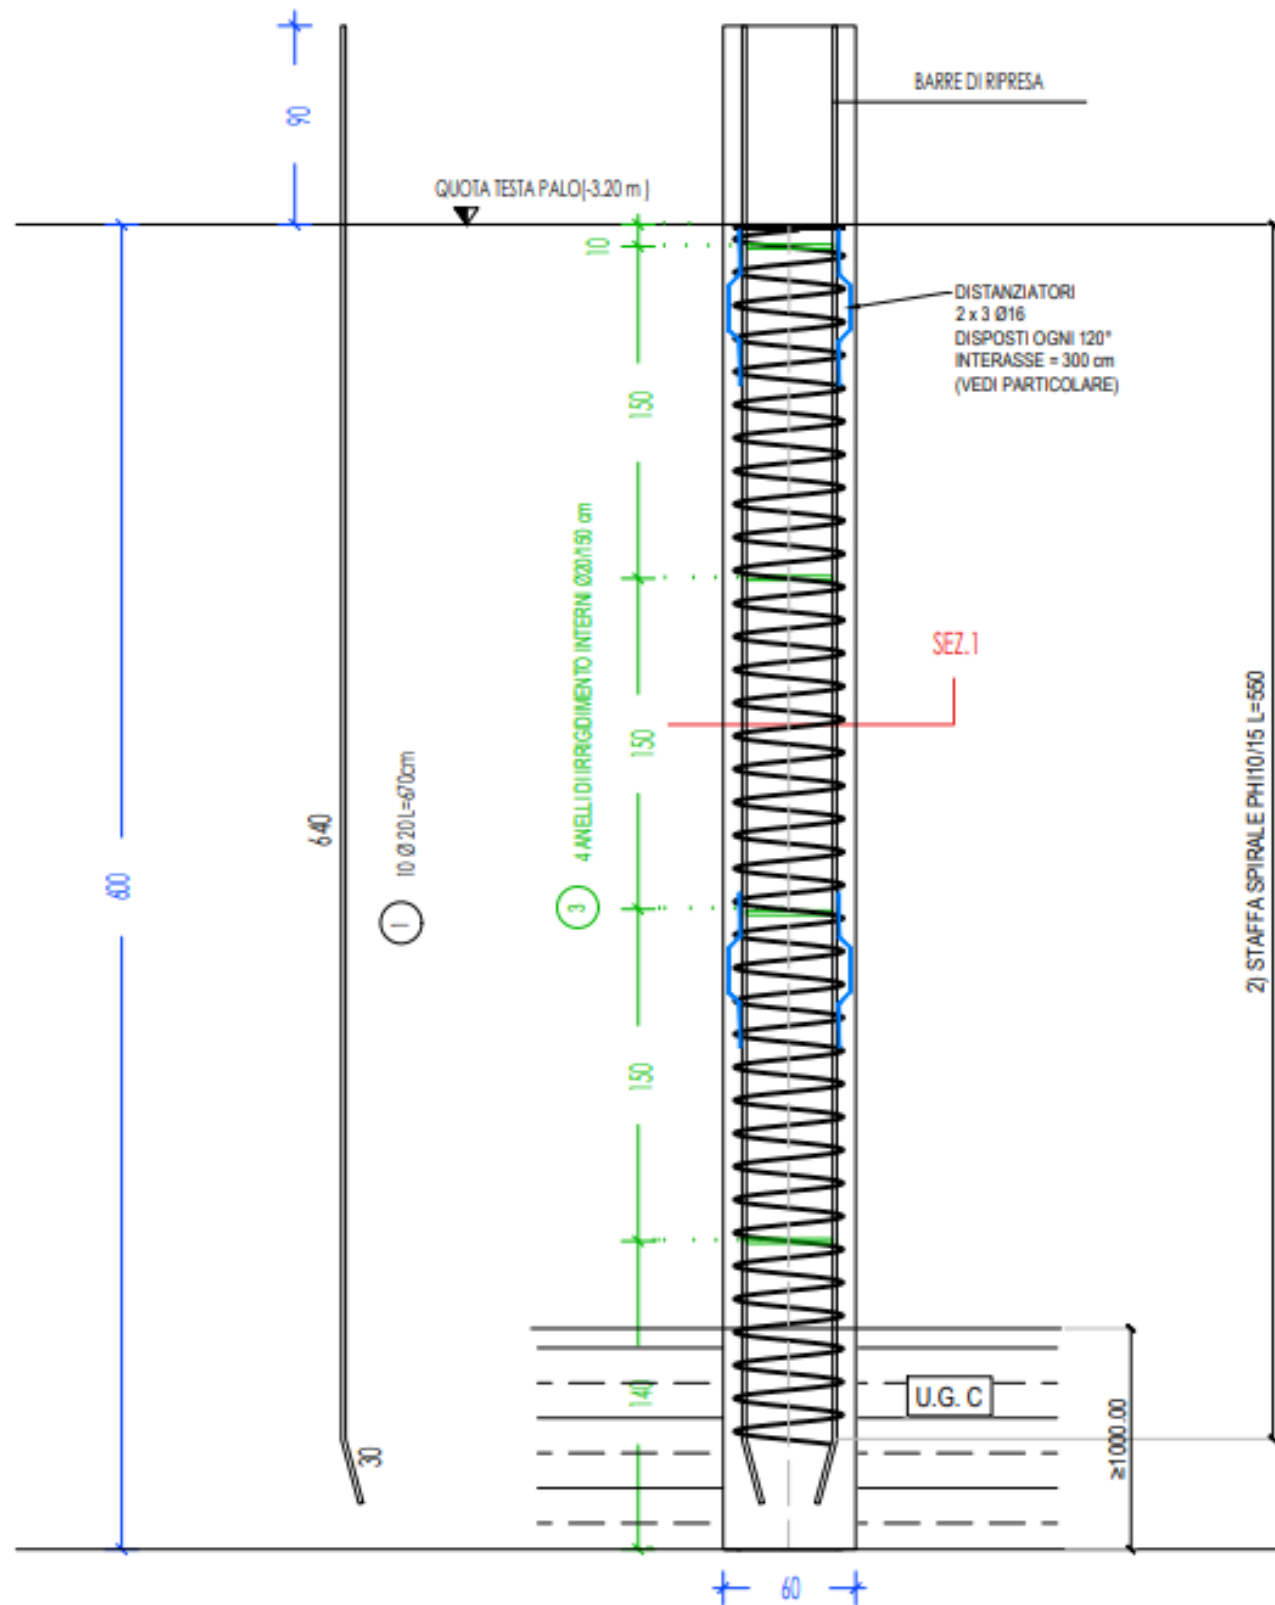


ARMATURA PALI Ø600 L = 6 m

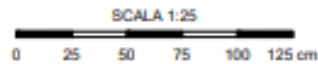

| COORDINATE PALI | | | | |
|-----------------|------------|------------|-------|-----|
| | | | | |
| N. PALO | X | Y | ØPALO | L |
| | [m] | [m] | [mm] | [m] |
| 87 | 512480.859 | 4349549.69 | 600 | 6 |

Quota testa palo (scapitozzatura): +51,70 m

Quota imposta fondazione: + 50,80 m

