
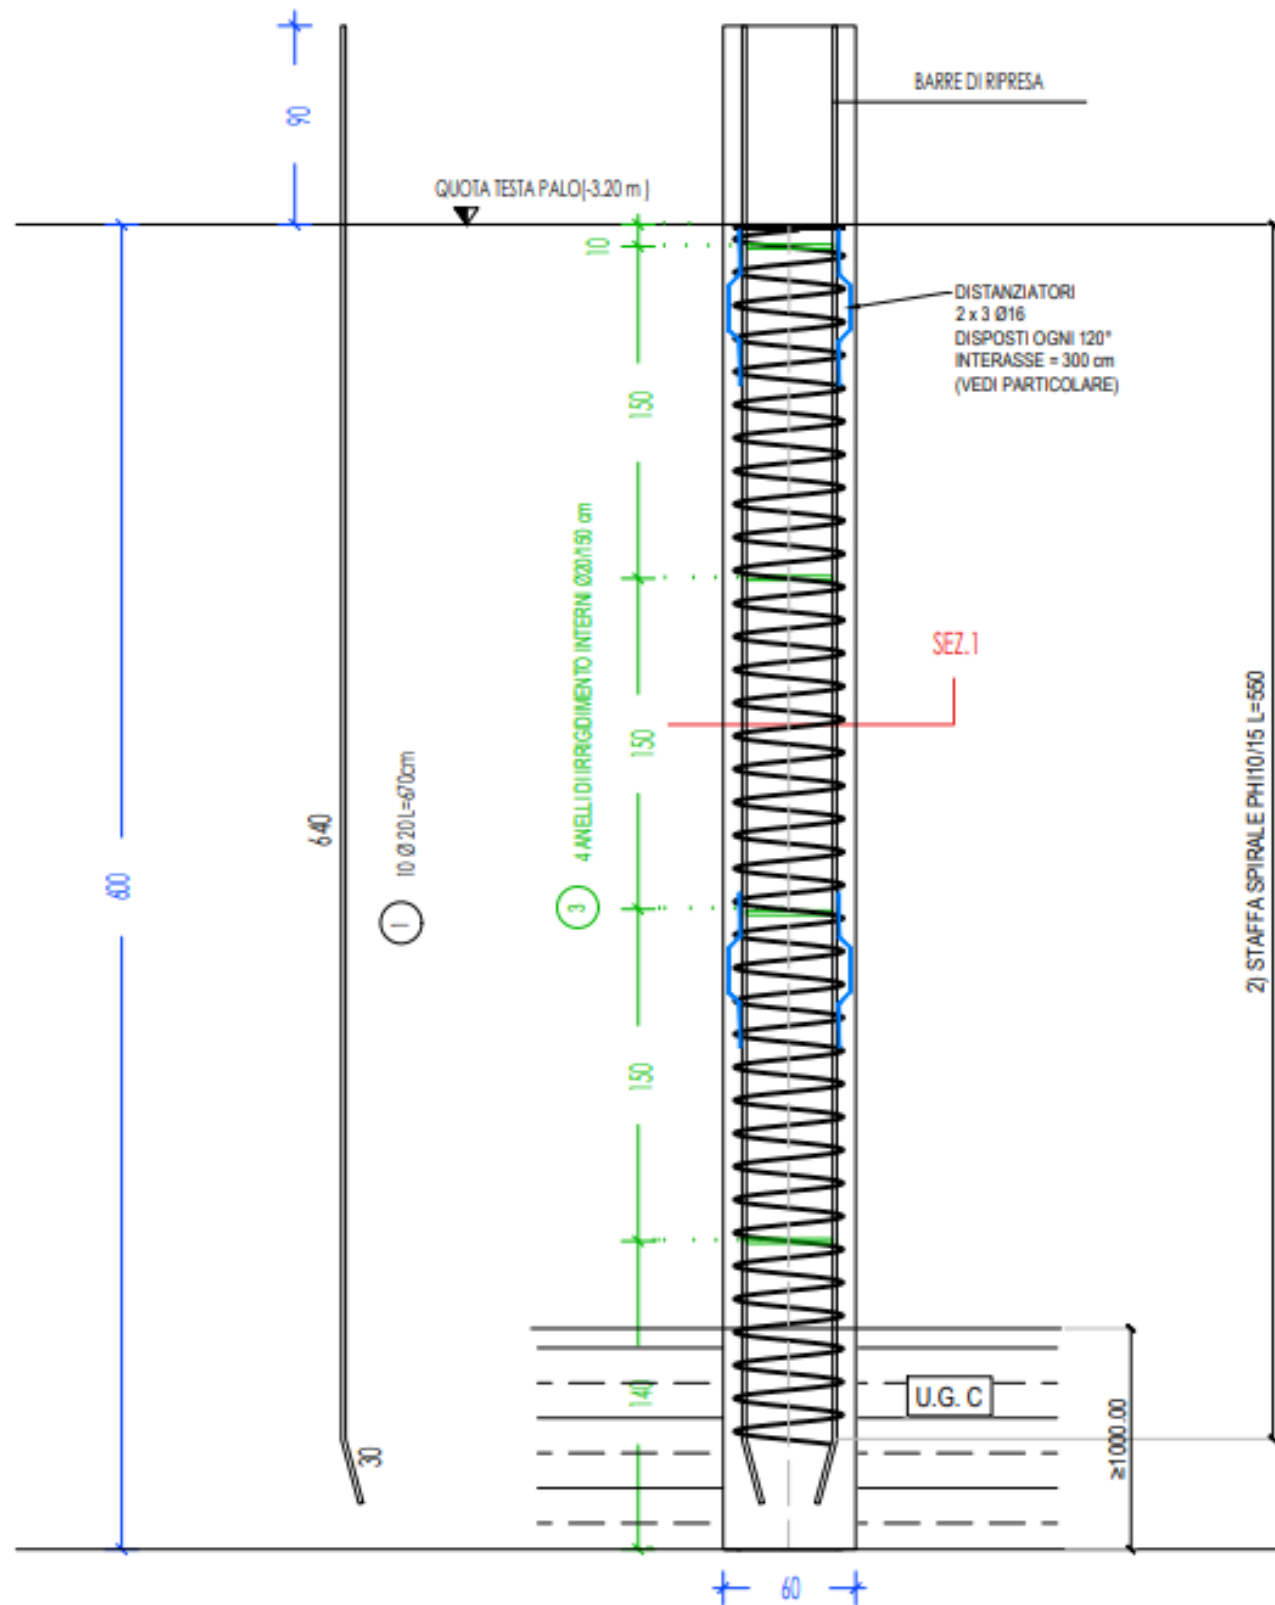


ARMATURA PALI Ø600 L = 6 m

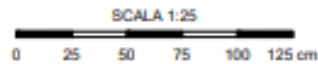

| COORDINATE PALI |            |            |       |     |
|-----------------|------------|------------|-------|-----|
| N. PALO         | X          | Y          | ØPALO | L   |
|                 | [m]        | [m]        | [mm]  | [m] |
| 104             | 512488.226 | 4349530.36 | 600   | 6   |

Quota testa palo (scapitozzatura): +51,70 m

Quota imposta fondazione: + 50,80 m

