

ARMATURA PALI Ø600 L = 6 m

SCALA 1:25
0 25 50 75 100 125 cm




COORDINATE PALI

N. PALO	X	Y	ØPALO	L
	[m]	[m]	[mm]	[m]
10	512450.027	4349523.769	600	6

Quota testa palo (scapitozzatura): +51,70 m

Quota imposta fondazione: + 50,80 m

SEZIONE 1

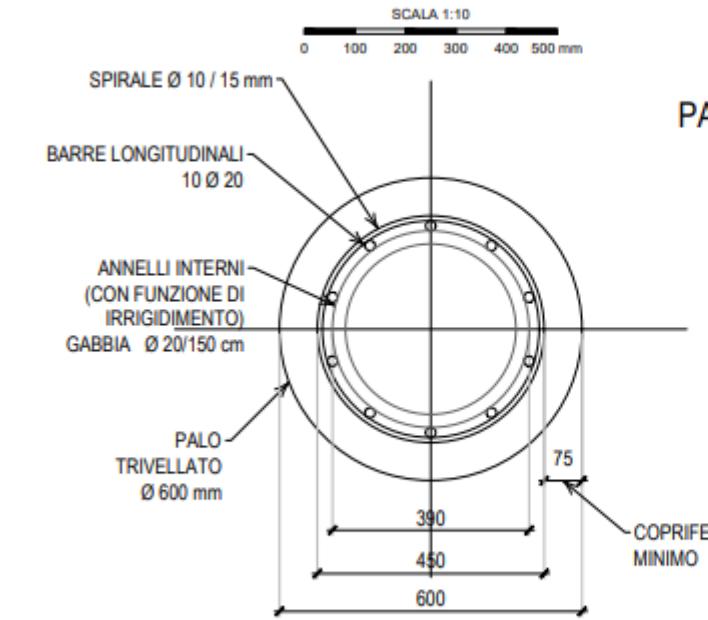

PARTICOLARE DISTANZIATORI

