
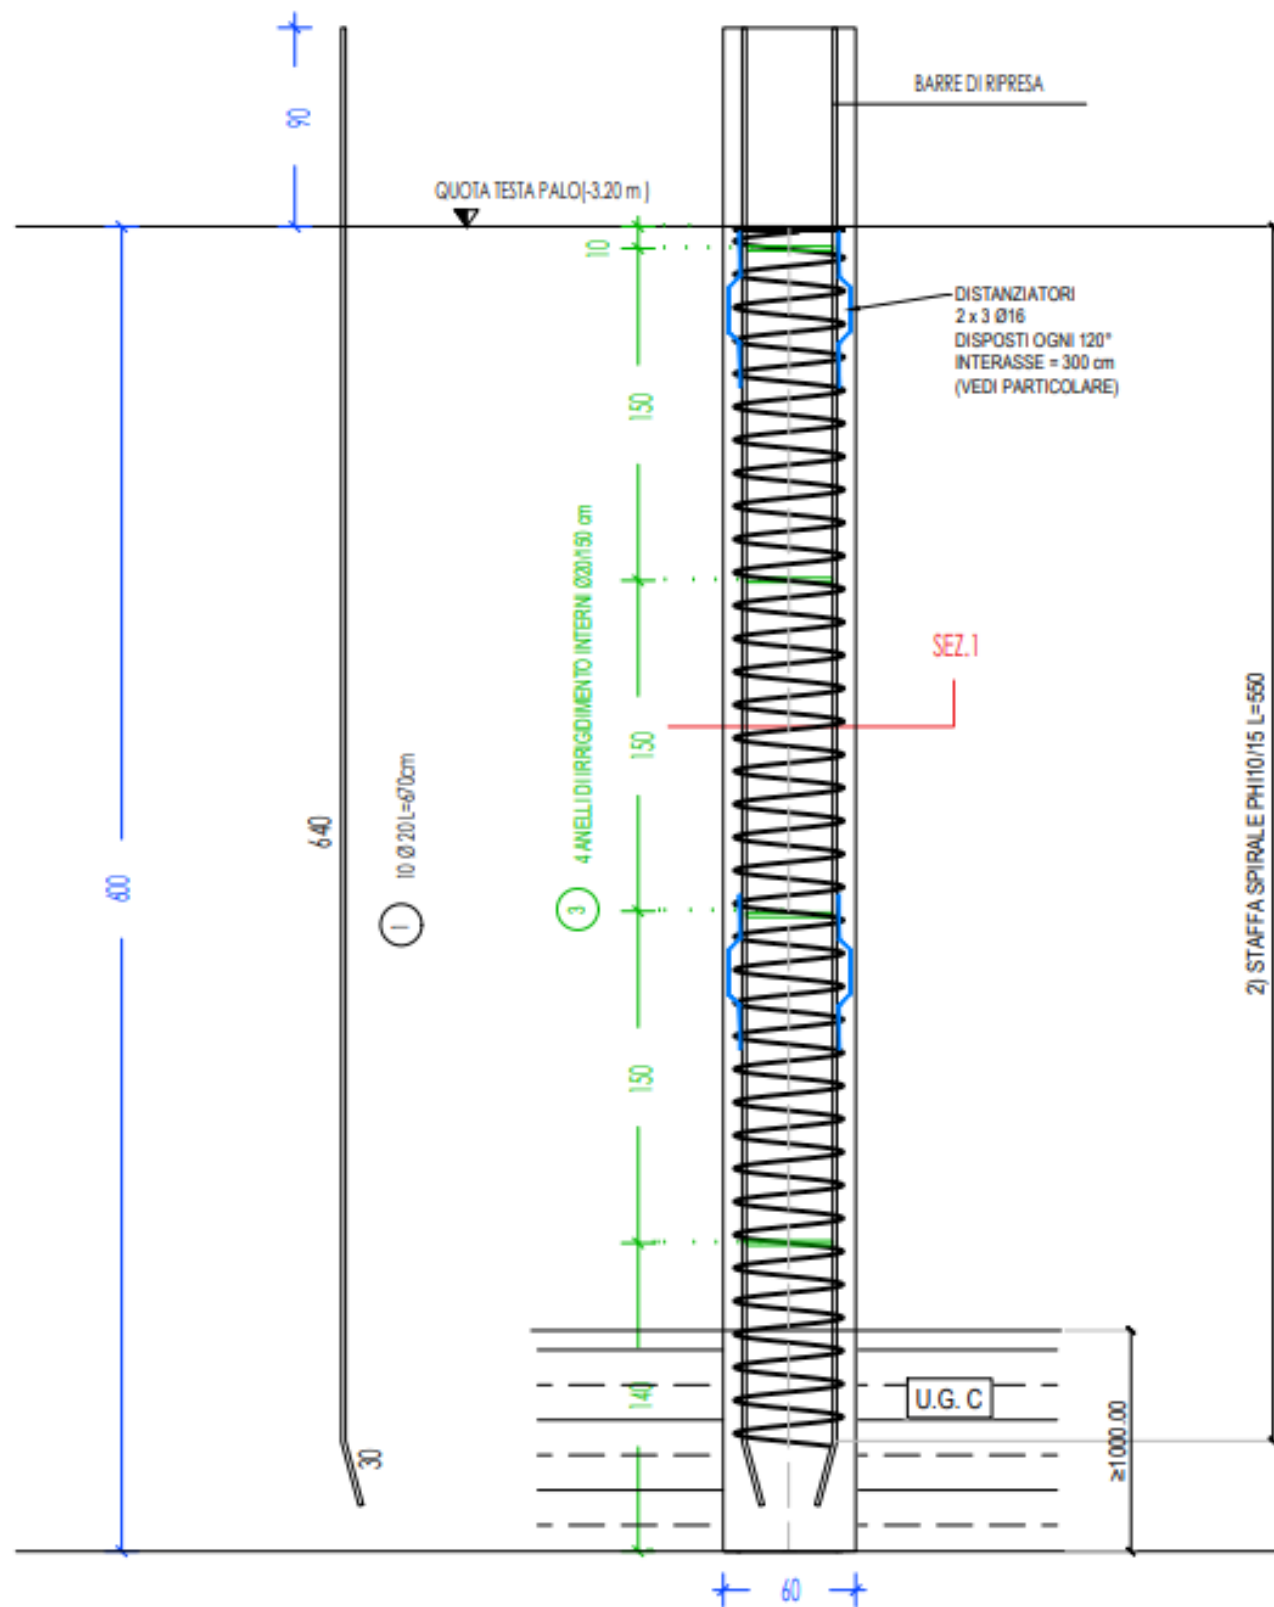


ARMATURA PALI Ø600 L = 6 m

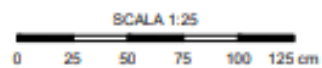

COORDINATE PALI				
N. PALO	X	Y	ØPALO	L
	[m]	[m]	[mm]	[m]
18	512455.786	4349517.291	600	6

Quota testa palo (scapitozzatura): +51,70 m

Quota imposta fondazione: + 50,80 m

