


ARMATURA PALI Ø600 L = 6 m

SCALA 1:25

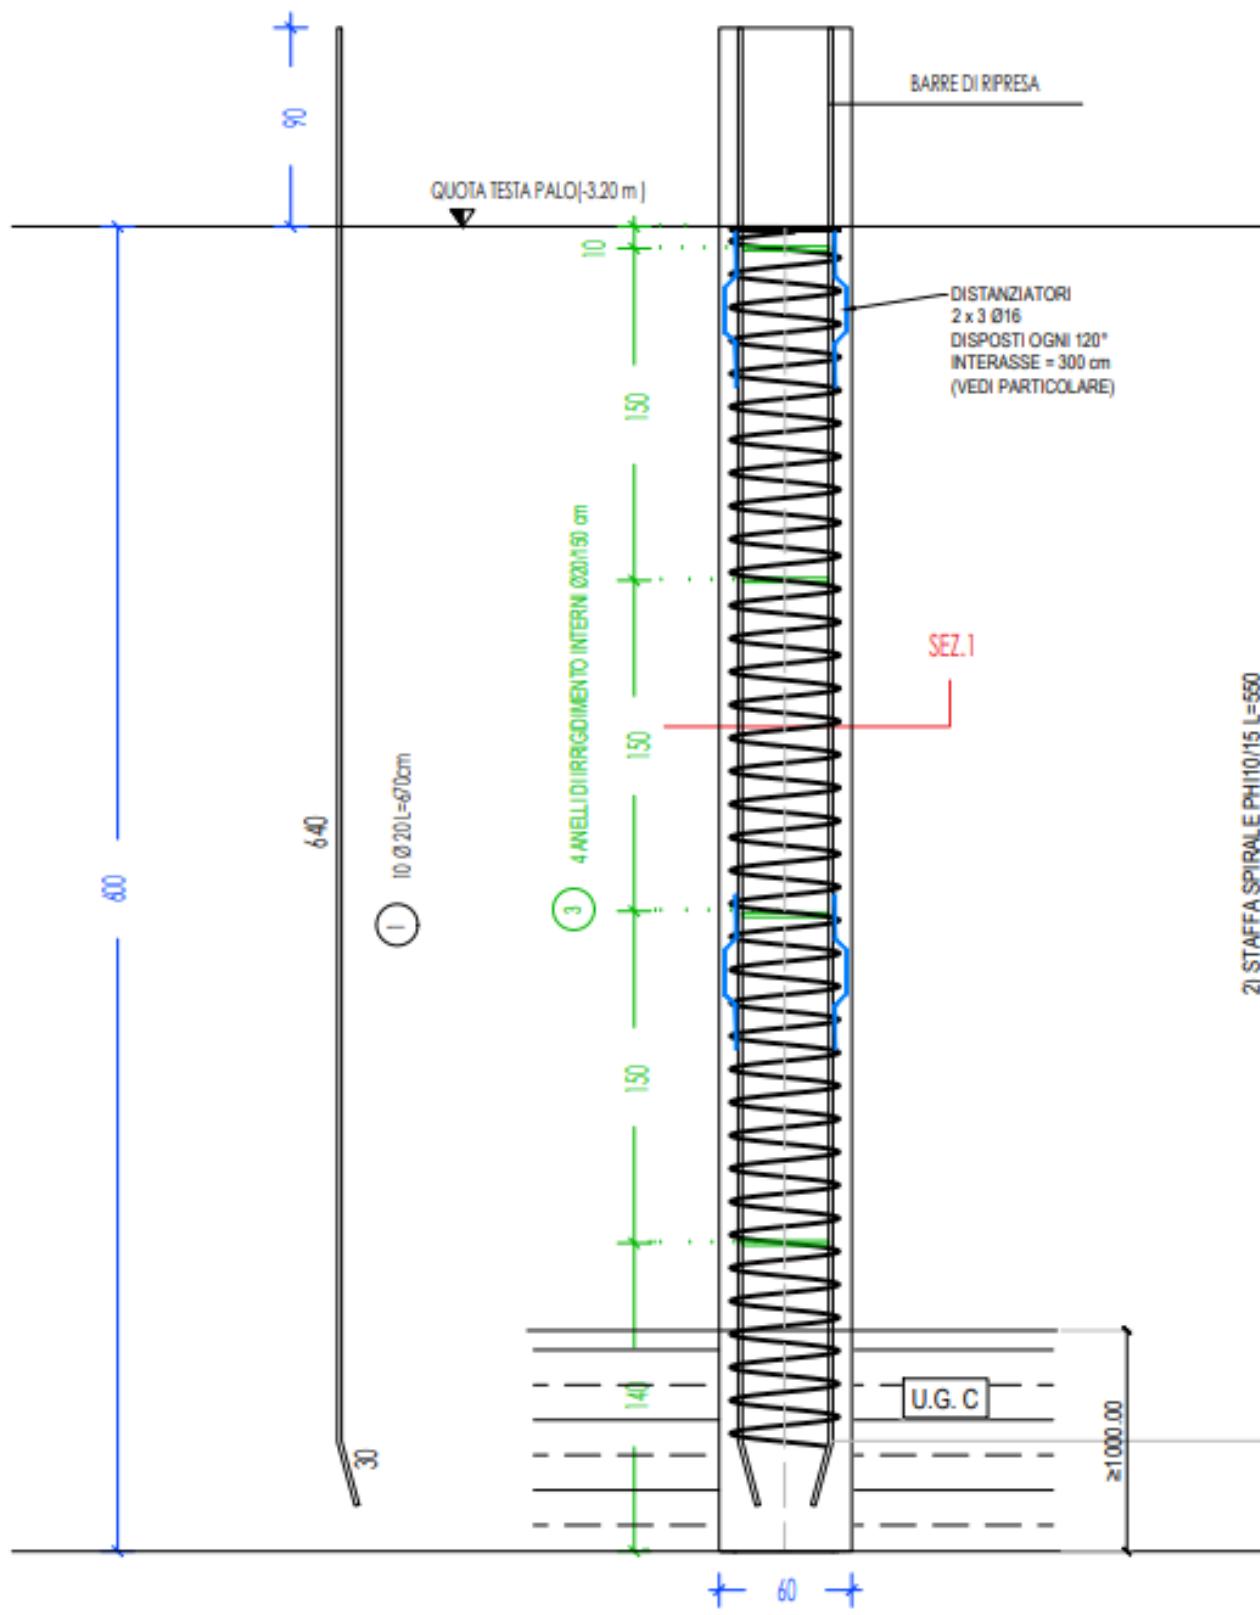

COORDINATE PAL

N. PALO	X [m]	Y [m]	ØPALO [mm]	L [m]
80	512482.246	4349519.5	600	6

Quota testa palo (scapitozzatura): +51,70 m

Quota imposta fondazione: + 50,80 m

