


ARMATURA PALI Ø600 L = 6 m

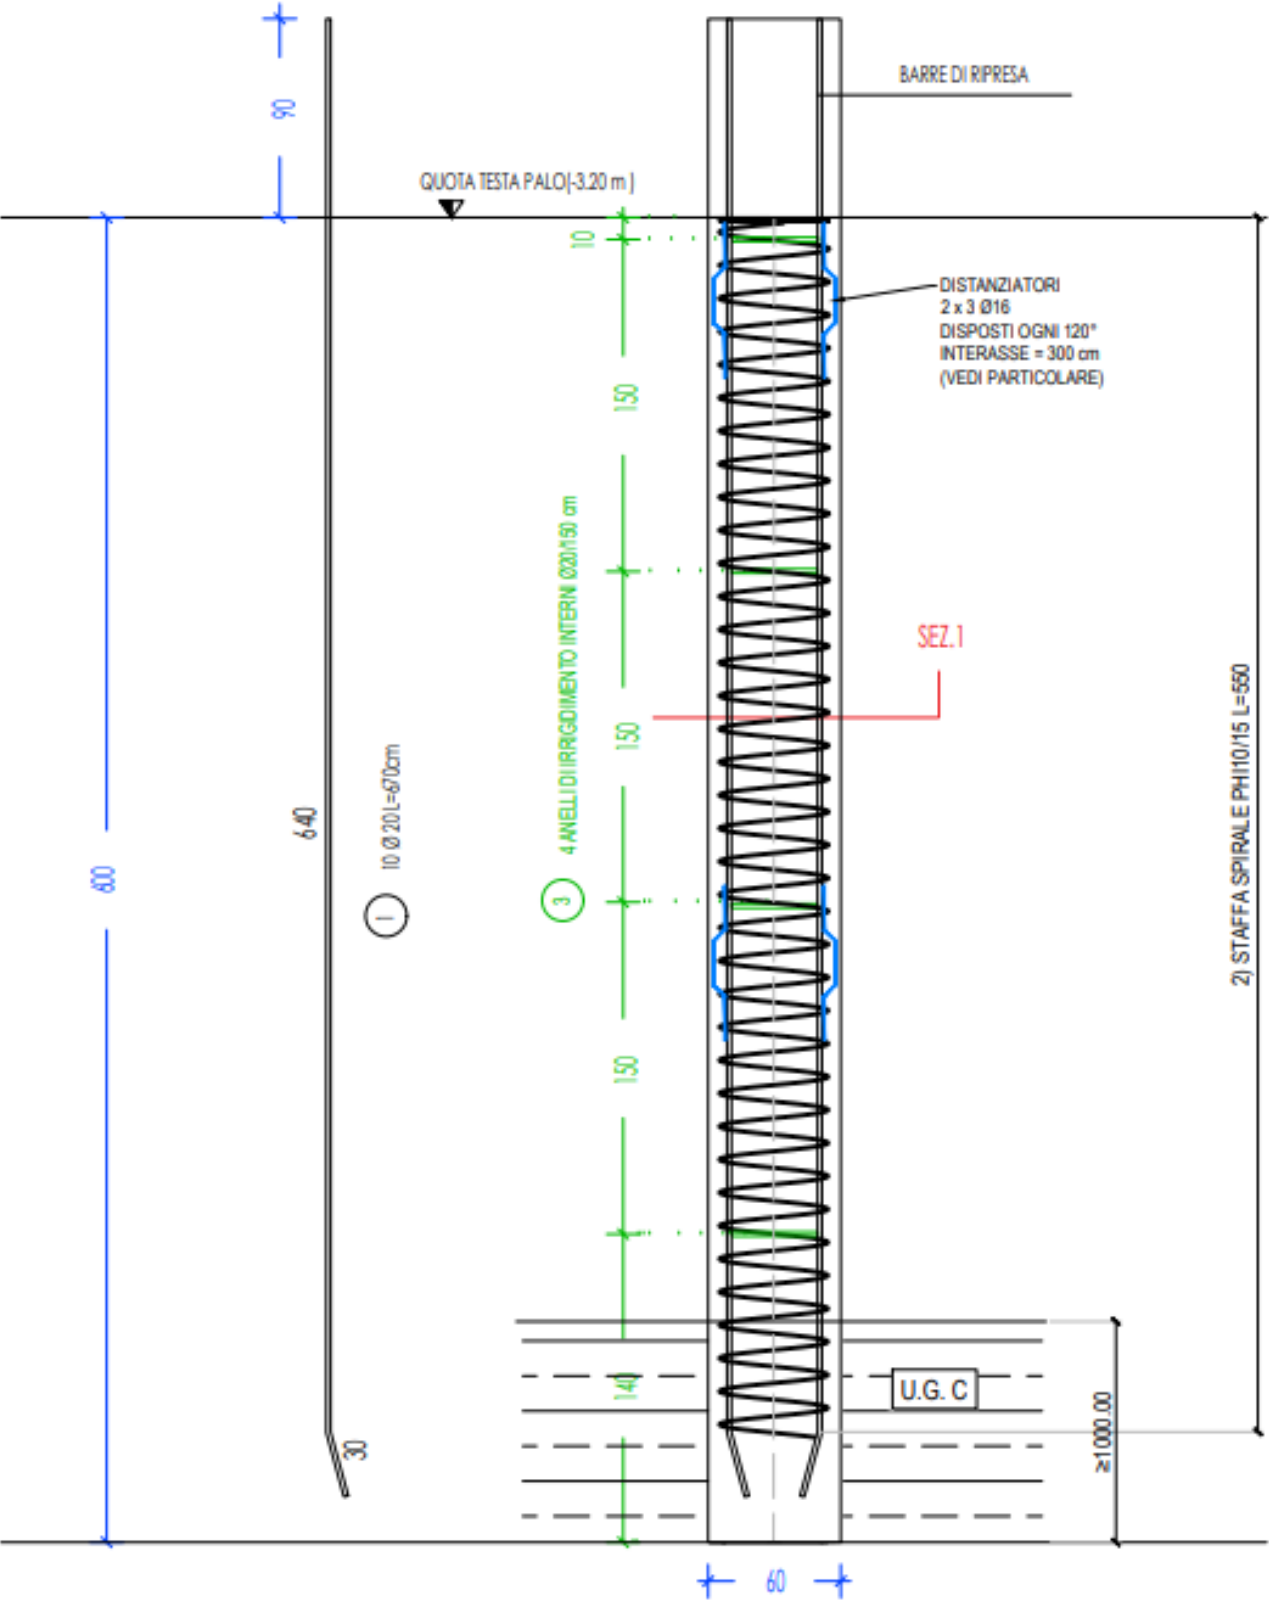



COORDINATE PALI

| N. PALO | X          | Y           | ØPALO | L   |
|---------|------------|-------------|-------|-----|
|         | [m]        | [m]         | [mm]  | [m] |
| 20      | 512458.112 | 4349516.682 | 600   | 6   |

Quota testa palo (scapitozzatura): +51,70 m

Quota imposta fondazione: + 50,80 m

SEZIONE 1

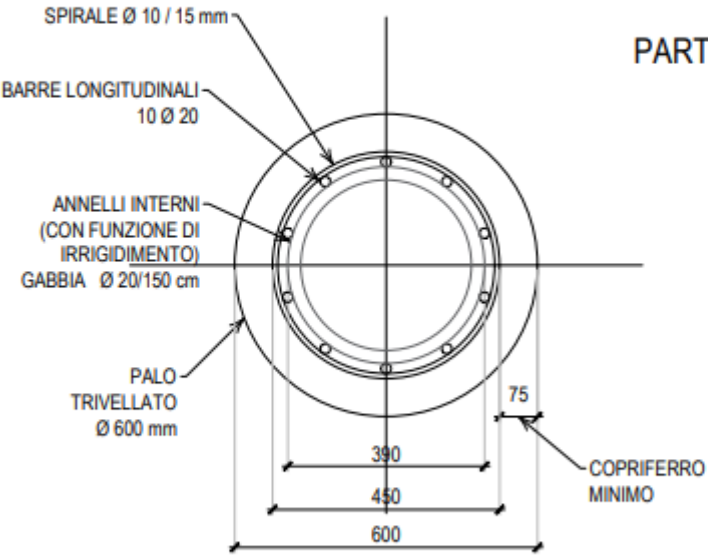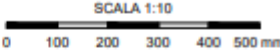

PARTICOLARE DISTANZIATORI

