


ARMATURA PALI Ø600 L = 6 m

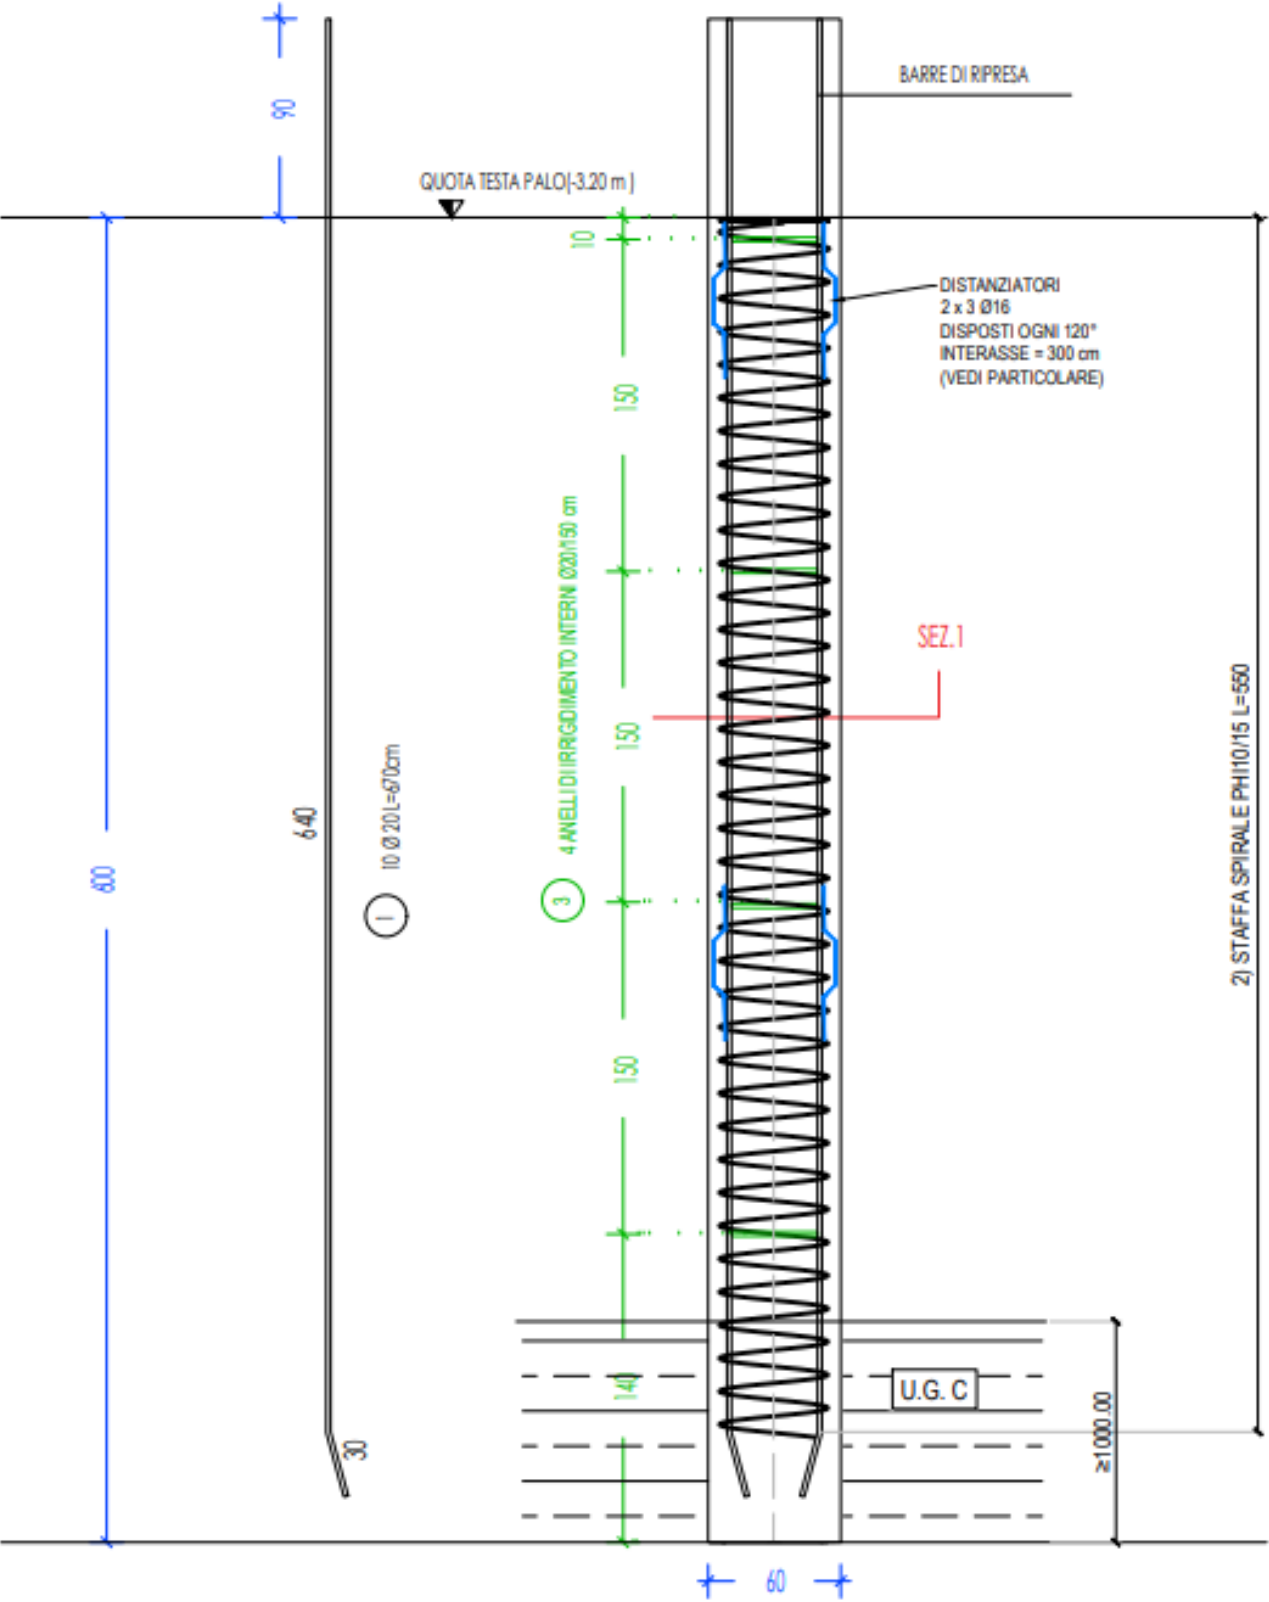



COORDINATE PALI

N. PALO	X [m]	Y [m]	ØPALO [mm]	L [m]
52	512470.968	4349519.16	600	6

Quota testa palo (scapitozzatura): +51,70 m

Quota imposta fondazione: + 50,80 m

SEZIONE 1

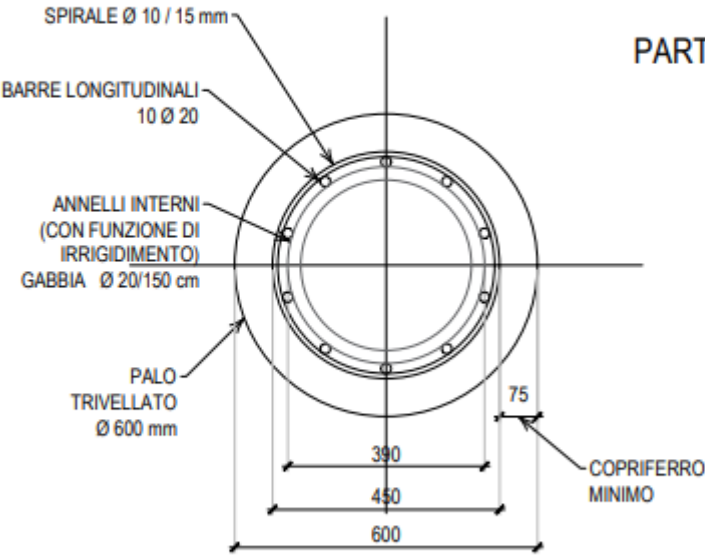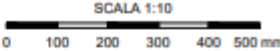

PARTICOLARE DISTANZIATORI

